




INTERIOR PROJECT OF
THE FACULTY OF EARTH & ENVIRONMENTAL SCIENCE
AND ENGINEERING & TECHNOLOGY BUILDING,
UNIVERSITY OF DHAKA.

Prepared by: **arch INNER**

18th December, 2024

Its **core task** and emphasizes it the most. The design work of the project is segregated in to a framework of **Seven (07)** stages, that encompass all tasks and responsibilities of the useful completion of the project.

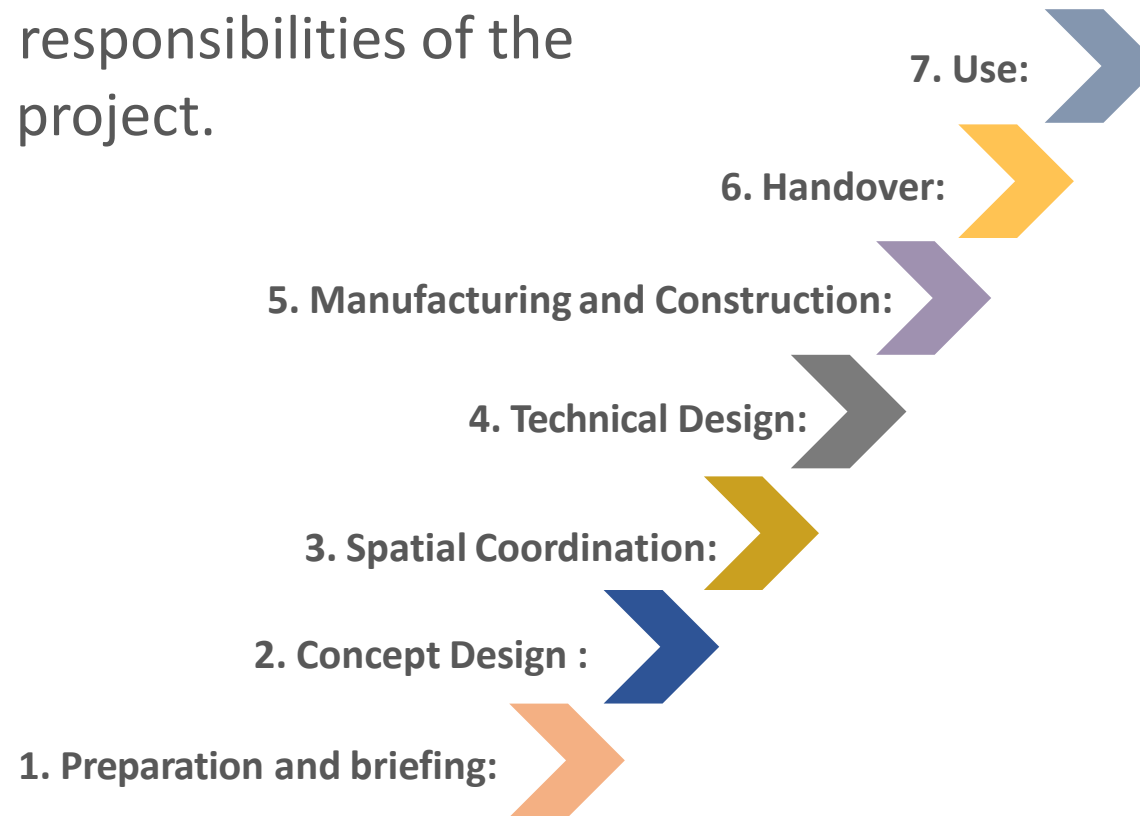






Usually we are follow the local good practice.

WORK STRATEGY PLAN



H- 3&5, R- 07,
Gulshan-badda
link Road,Dhaka-1212.

M: +880 1717038194
E: archinner@gmail.com
W: www.archinner.com

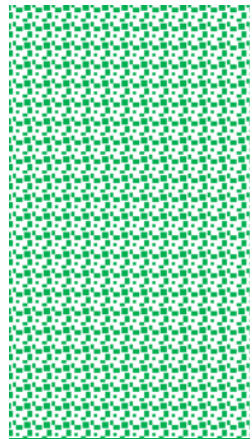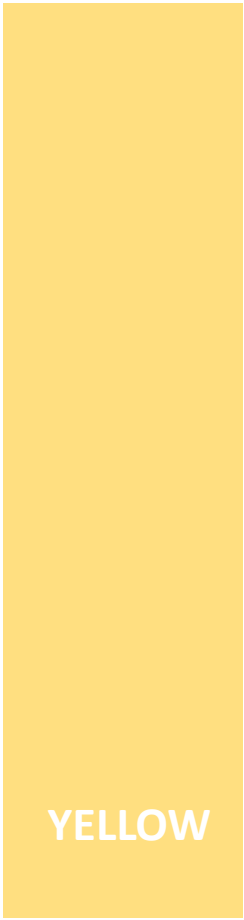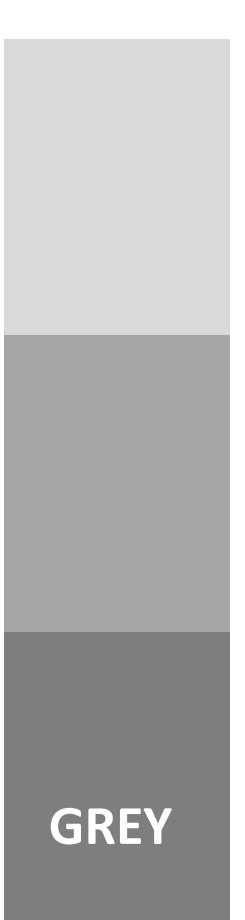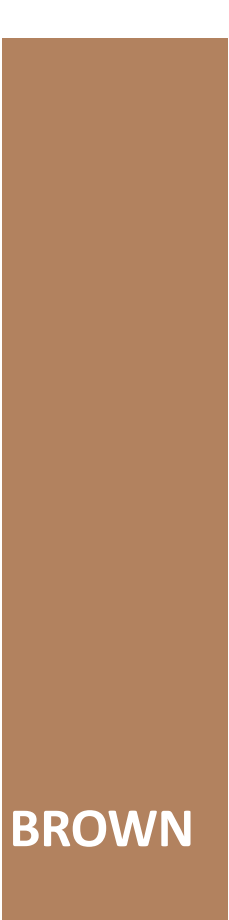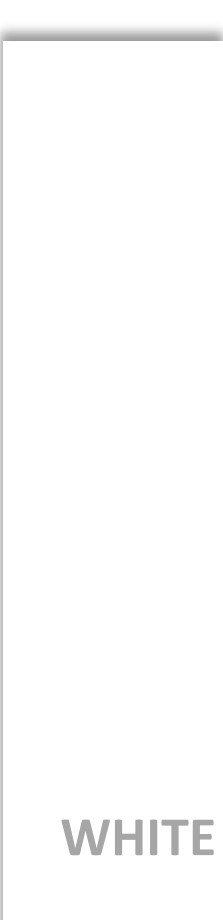 GREEN • Long work hour • Gentle • Stimulation • Health boost	 YELLOW • Long work hour • Adds right and cheerful vibe • Stimulate positivity, creativity, happiness	 GREY • Flexibility • Liven things up • Compliments other colors • Neutralized extreme	 BROWN • Warmth & supportive • Earthy color • Signifies being industrious & steadfast	 WOOD • Sensuous • Relaxing • elegance	 WHITE • Sense of balance and neutrality • Purity and cleanliness • elegance
---	---	--	---	--	--


SELECTION OF MODE BOARD



H- 3&5, R- 07,
Gulshan-badda
link Road, Dhaka-1212.

M: +880 1717038194
E: archinner@gmail.com
W: www.archinner.com

FLOOR FINISH REFERENCE

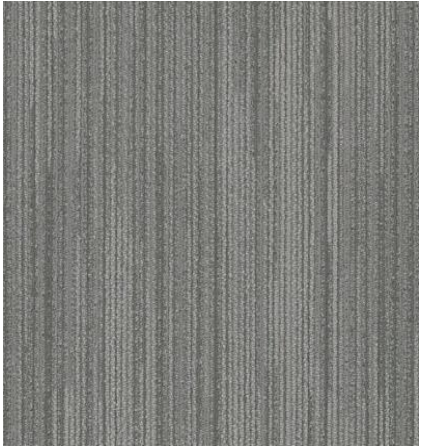

FLOOR FINISH: FLOTEX & TUFFTED CARPET



FLOOR FINISH: VINYL, EPOXY & CERAMIC TILES





H- 3&5, R- 07,
Gulshan-badda
link Road,Dhaka-1212.

M: +880 1717038194
E: archinner@gmail.com
W: www.archinner.com



WALL FINISH: ACOUSTIC PANEL

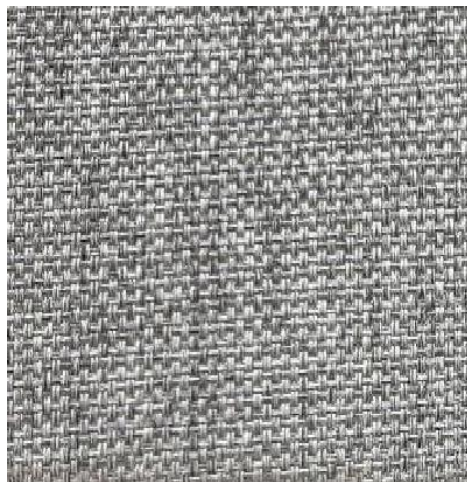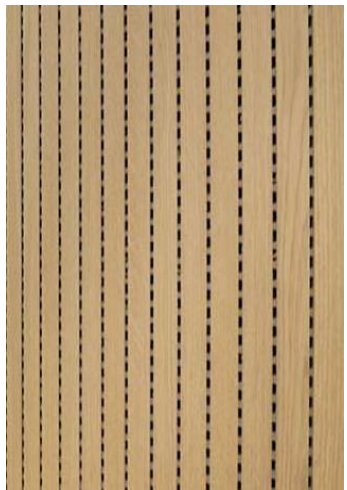

WALL FINISH: FABRIC PANEL, ROYAL & TEXTURE PAINT





WALL FINISH REFERENCE



H- 3&5, R- 07,
Gulshan-badda
link Road,Dhaka-1212.

M: +880 1717038194
E: archinner@gmail.com
W: www.archinner.com

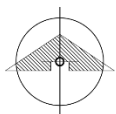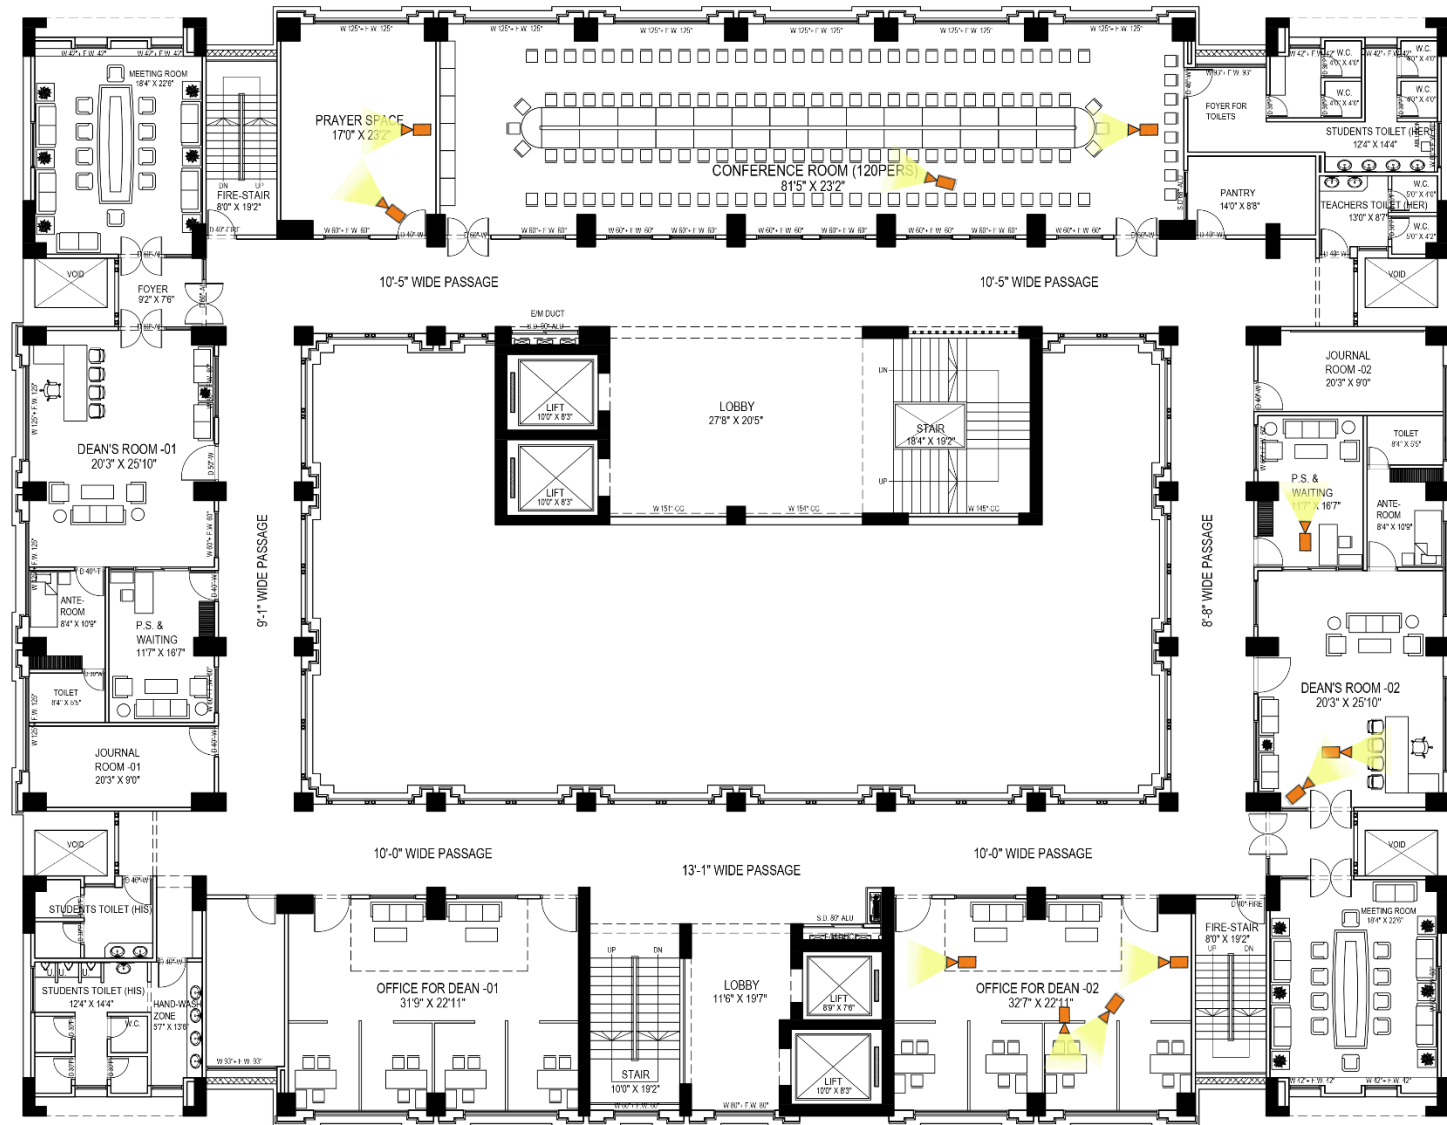

2ND FLOOR PLAN

FLOOR AREA : 15,650 SFT

SECOND FLOOR PLAN

TOTAL FLOOR AREA
15,650 SFT.



H- 3&5, R- 07,
Gulshan-badda
link Road,Dhaka-1212.

M: +880 1717038194
E: archinner@gmail.com
W: www.archinner.com

INTERIOR VIEW (3D)

DEAN ROOM



2ND FLOOR PLAN
1:1000 (A4, 10/10/10)



H- 3&5, R- 07,
Gulshan-badda
link Road,Dhaka-1212.


M: +880 1717038194
E: archinner@gmail.com
W: www.archinner.com





INTERIOR VIEW (3D)

DEAN ROOM

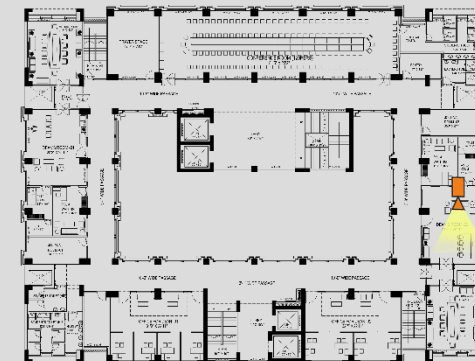

2ND FLOOR PLAN
P-1024-0004, 0008-01




H- 3&5, R- 07,
Gulshan-badda
link Road,Dhaka-1212.

M: +880 1717038194
E: archinner@gmail.com
W: www.archinner.com



INTERIOR VIEW (3D)

DEAN ROOM

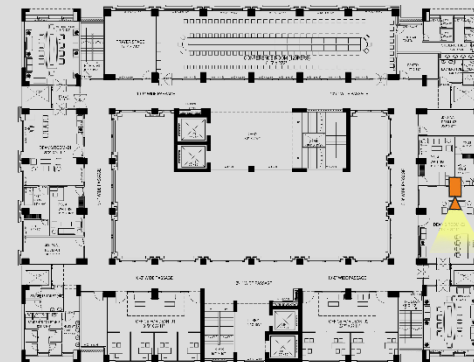

2ND FLOOR PLAN
P-1024-0004, 0000-01



H- 3&5, R- 07,
Gulshan-badda
link Road,Dhaka-1212.


M: +880 1717038194

E: archinner@gmail.com

W: www.archinner.com

INTERIOR VIEW (3D)

DEAN WAITING

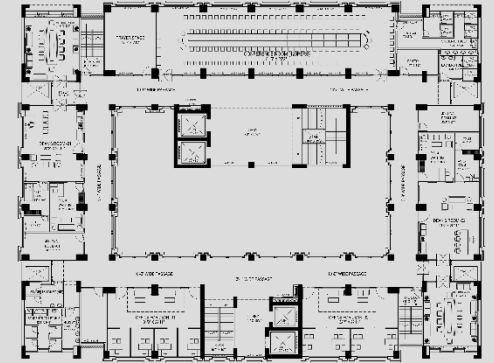

2ND FLOOR PLAN
P-1024-40054_10000000




H- 3&5, R- 07,
Gulshan-badda
link Road,Dhaka-1212.

M: +880 1717038194
E: archinner@gmail.com
W: www.archinner.com



INTERIOR VIEW (3D) OFFICER'S FOR DEAN

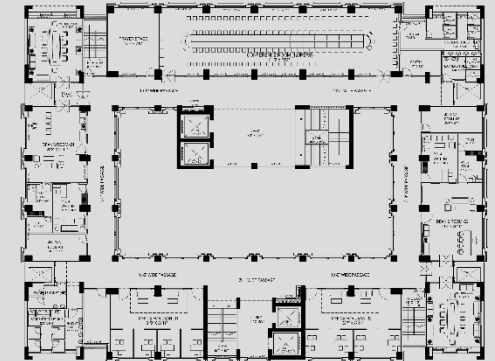


2ND FLOOR PLAN
P-1024-40054, 1000000




H- 3&5, R- 07,
Gulshan-badda
link Road,Dhaka-1212.

M: +880 1717038194
E: archinner@gmail.com
W: www.archinner.com

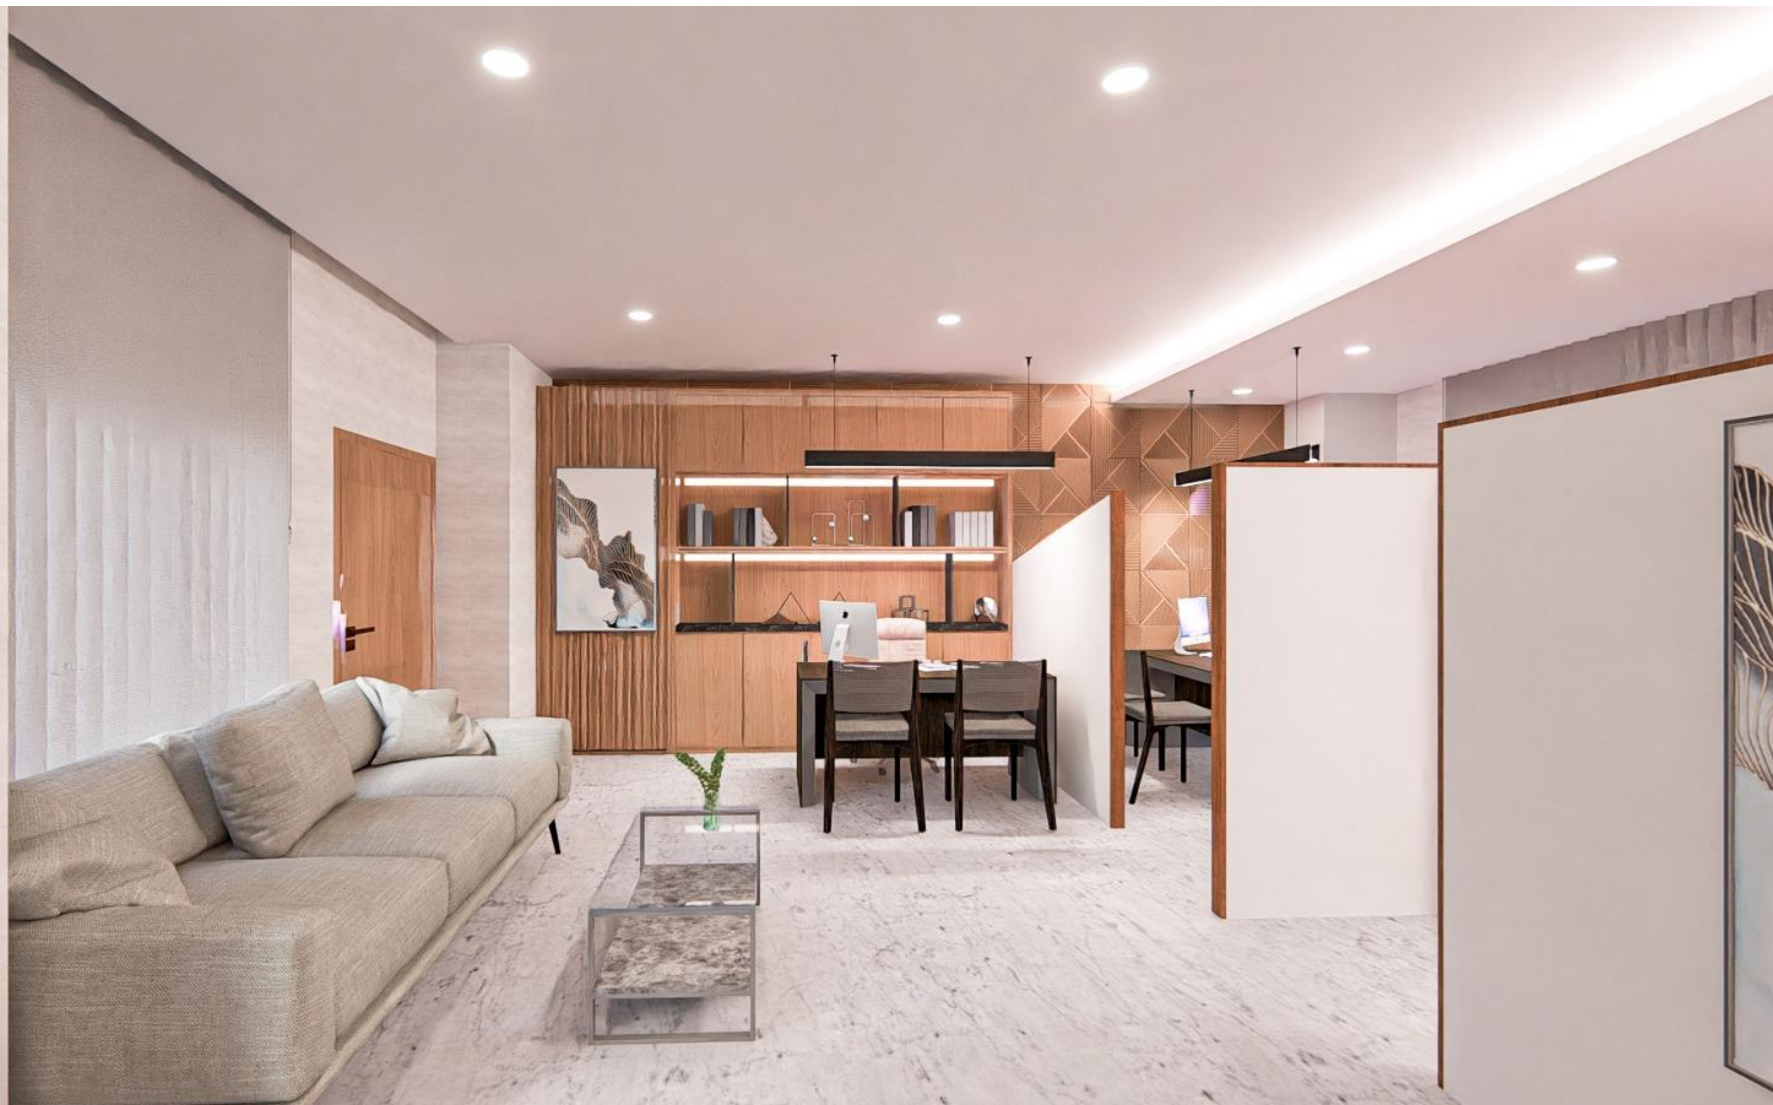

INTERIOR VIEW (3D) OFFICER'S FOR DEAN

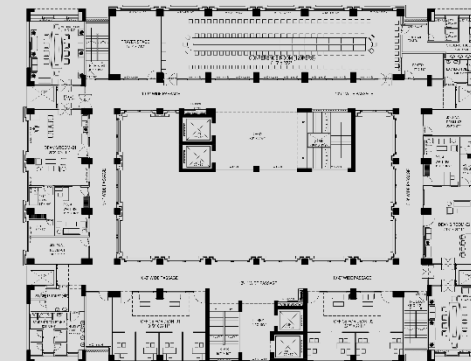

2ND FLOOR PLAN
P-1024-40054, 10024-011




H- 3&5, R- 07,
Gulshan-badda
link Road,Dhaka-1212.

M: +880 1717038194
E: archinner@gmail.com
W: www.archinner.com



INTERIOR VIEW (3D) OFFICER'S FOR DEAN

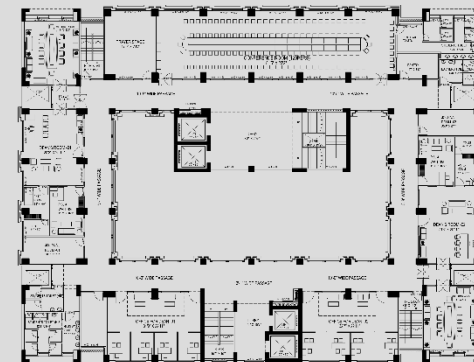

2ND FLOOR PLAN
P-1024-40054, 1000000000




H- 3&5, R- 07,
Gulshan-badda
link Road,Dhaka-1212.

M: +880 1717038194
E: archinner@gmail.com
W: www.archinner.com



INTERIOR VIEW (3D) OFFICER'S FOR DEAN

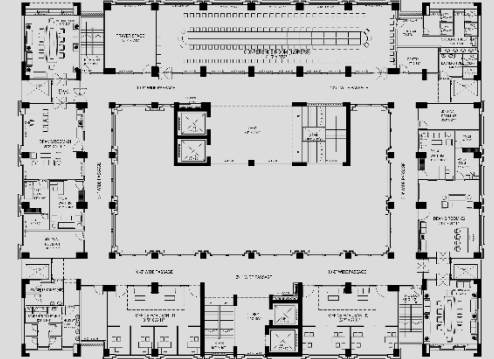

2ND FLOOR PLAN
P-1024-0004 10/08/17




H- 3&5, R- 07,
Gulshan-badda
link Road,Dhaka-1212.

M: +880 1717038194
E: archinner@gmail.com
W: www.archinner.com



INTERIOR VIEW (3D)

CONFERENCE ROOM

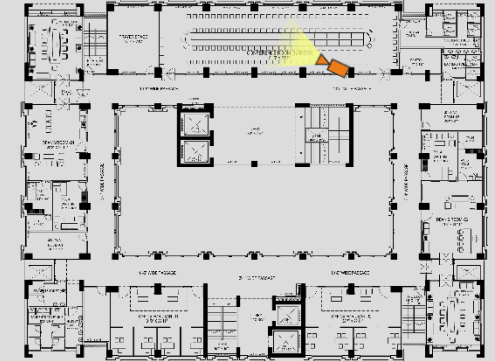

2ND FLOOR PLAN
+ CON AREA: 1012.01




H- 3&5, R- 07,
Gulshan-badda
link Road,Dhaka-1212.

M: +880 1717038194
E: archinner@gmail.com
W: www.archinner.com



INTERIOR VIEW (3D)

CONFERENCE ROOM

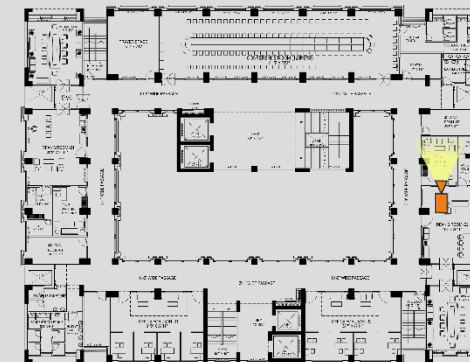

2ND FLOOR PLAN
FLOOR AREA: 15,000 SQ. FT.



H- 3&5, R- 07,
Gulshan-badda
link Road,Dhaka-1212.

M: +880 1717038194
E: archinner@gmail.com
W: www.archinner.com



INTERIOR VIEW (3D)

MEETING ROOM




3RD FLOOR PLAN
P:031-43FA 1:100 1/4"




H- 3&5, R- 07,
Gulshan-badda
link Road,Dhaka-1212.


M: +880 1717038194
E: archinner@gmail.com
W: www.archinner.com

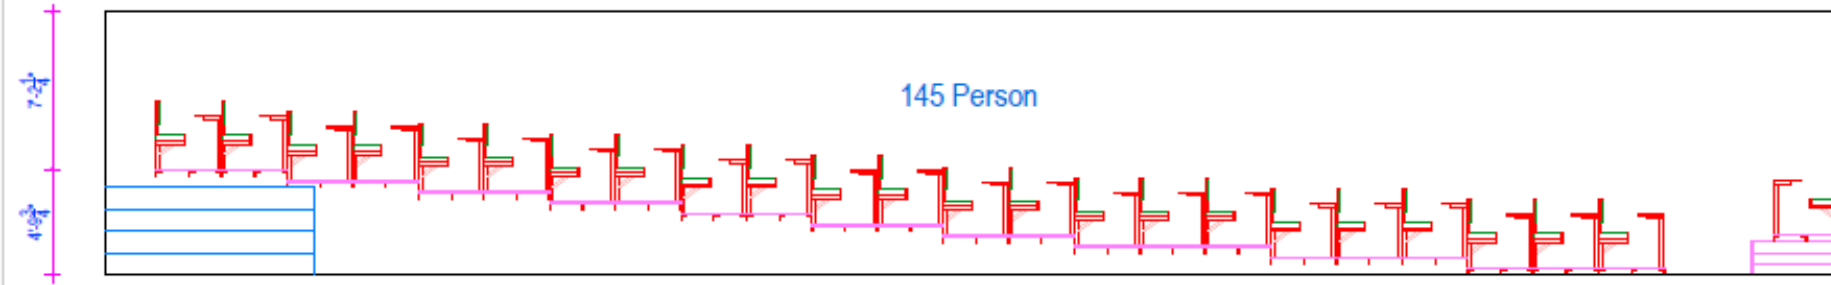

HALL ROOM SECTION

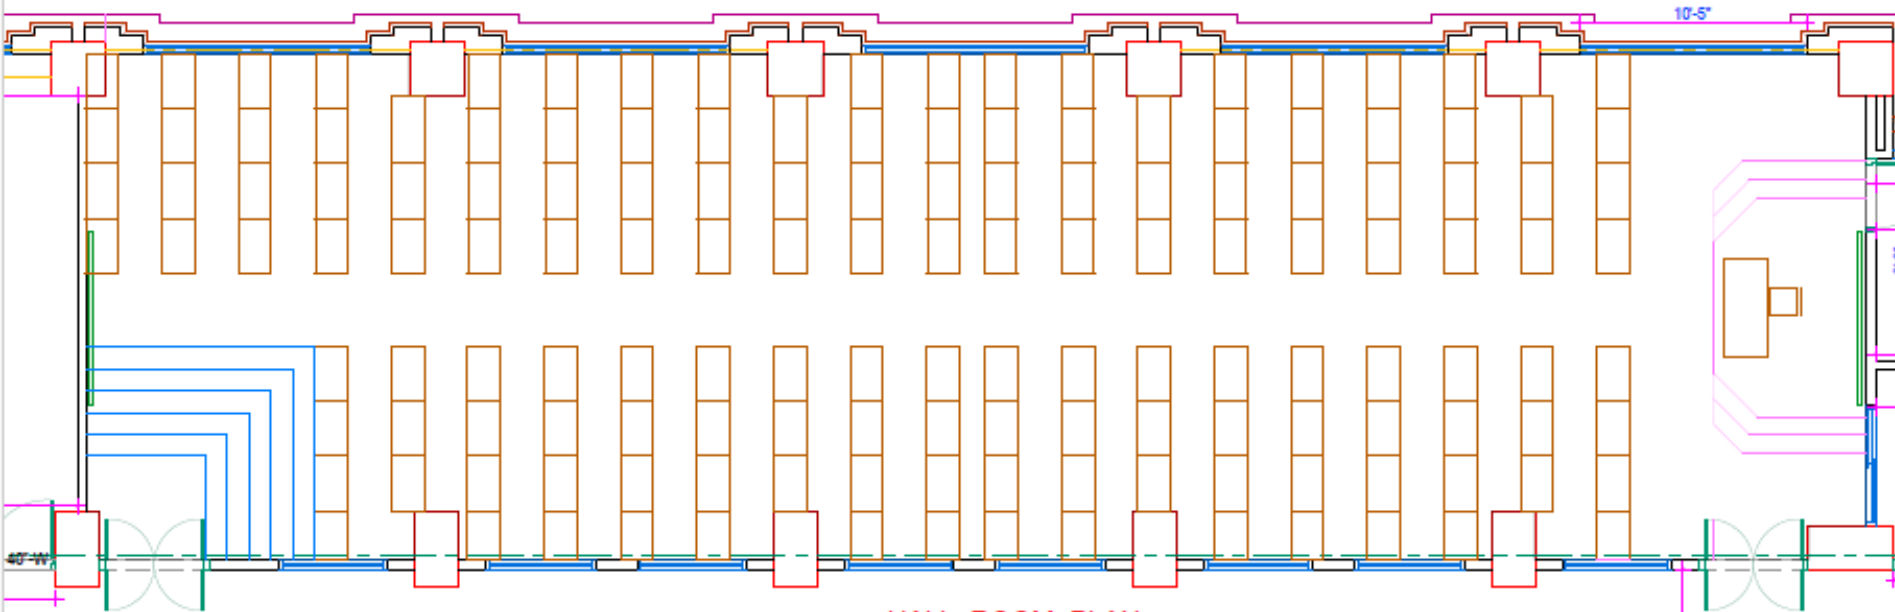

INTERIOR VIEW (3D) CONFERENCE ROOM

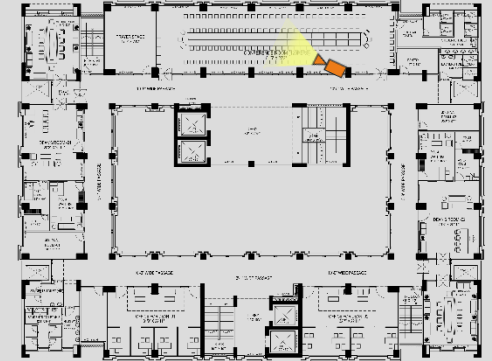

2ND FLOOR PLAN
+ CON AREA, 10128-01



H- 3&5, R- 07,
Gulshan-badda
link Road,Dhaka-1212.

M: +880 1717038194
E: archinner@gmail.com
W: www.archinner.com

KEW PERSONS :

Masud Rana Mihon

Bsc in Civil Engineering.

Mithun Chowdhury

Bsc in Civil Engineering.

IN CONSTRUCTION IMPLEMENTATION :

Ar. Mostafizur Rahman

Bachelor of Architecture

Ar. Redoy

Bachelor of Architecture

Md. Shamim Hossain

Bsc in Civil Engineering

Md. Taijul Islam

Diploma in Civil Engineering

Md. Abul Hossain

Diploma in Civil Engineering

MENTOR :

Ar. Lutfullahil Majid

B.Arch (BUET), IAB – M-76

OUR TEAM



H- 3&5, R- 07,
Gulshan-badda
link Road,Dhaka-1212.

M: +880 1717038194
E: archinner@gmail.com
W: www.archinner.com

THANK YOU

CONCLUSION



H- 3&5, R- 07,
Gulshan-badda
link Road,Dhaka-1212.

M: +880 1717038194
E: archinner@gmail.com
W: www.archinner.com